

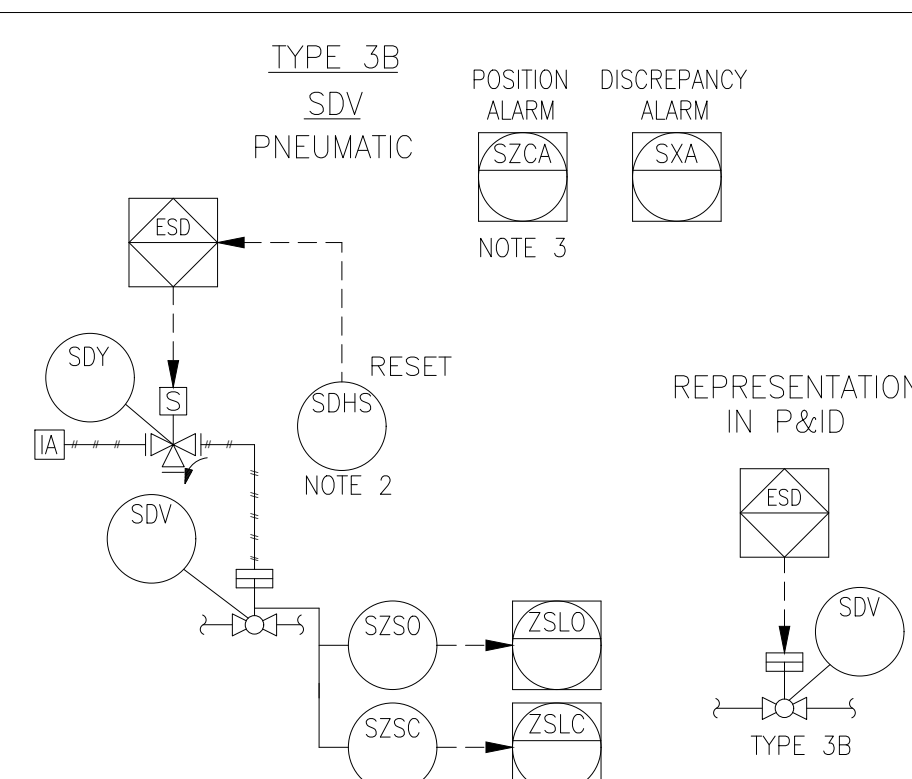
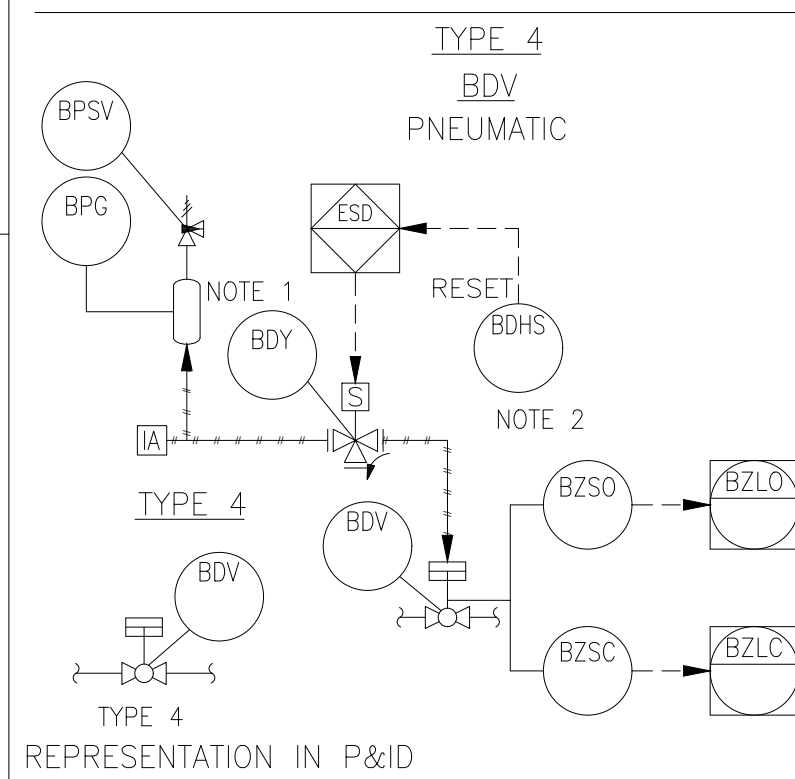
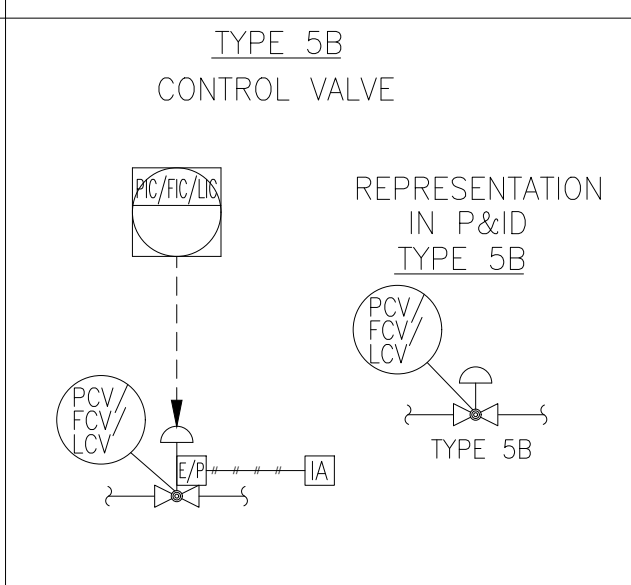
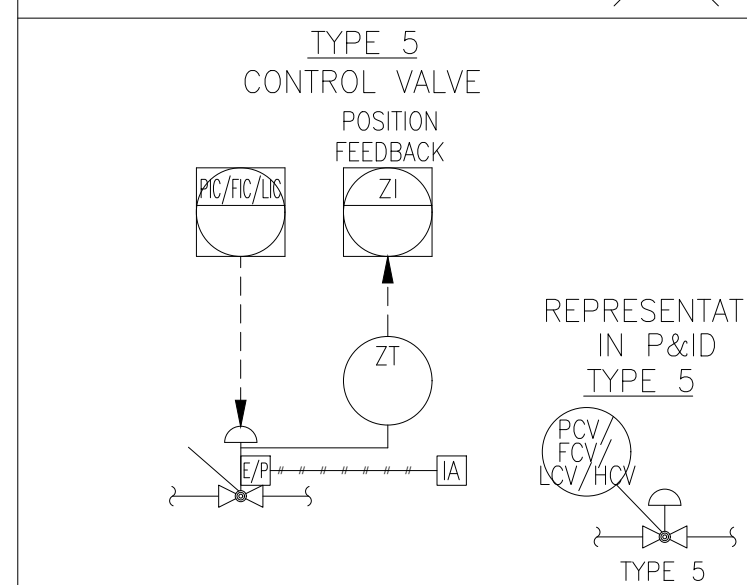
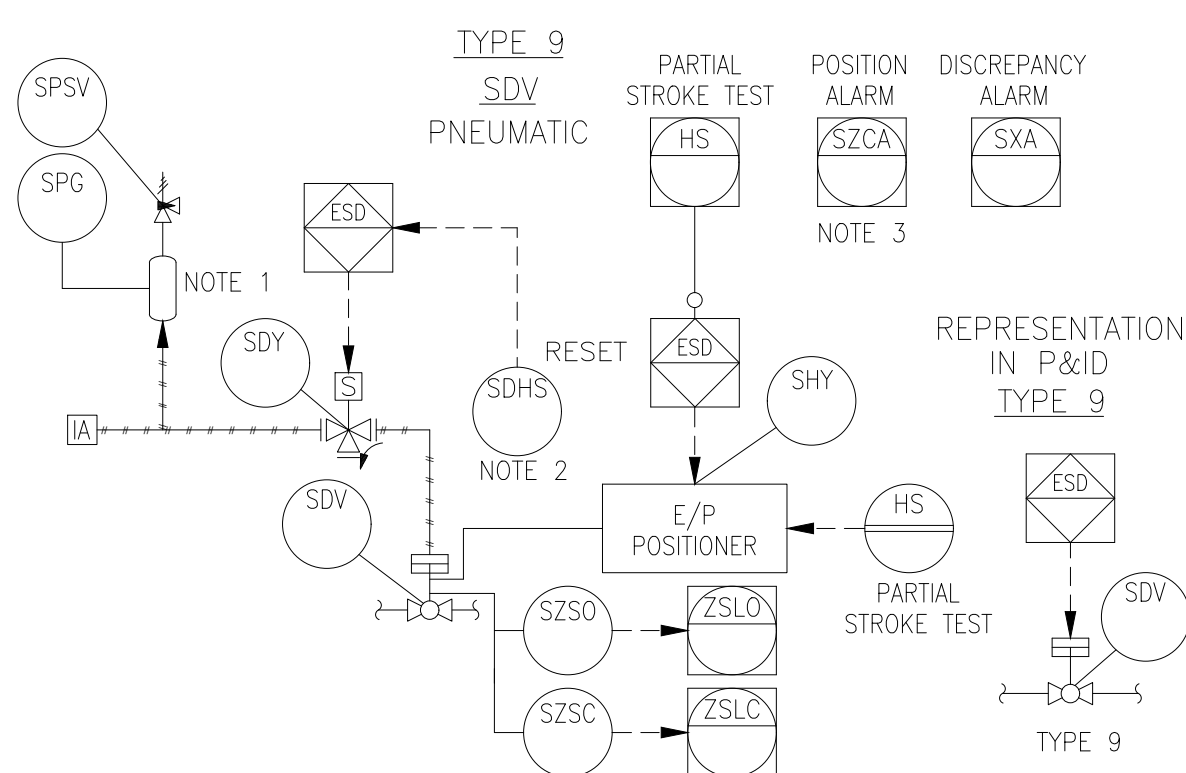
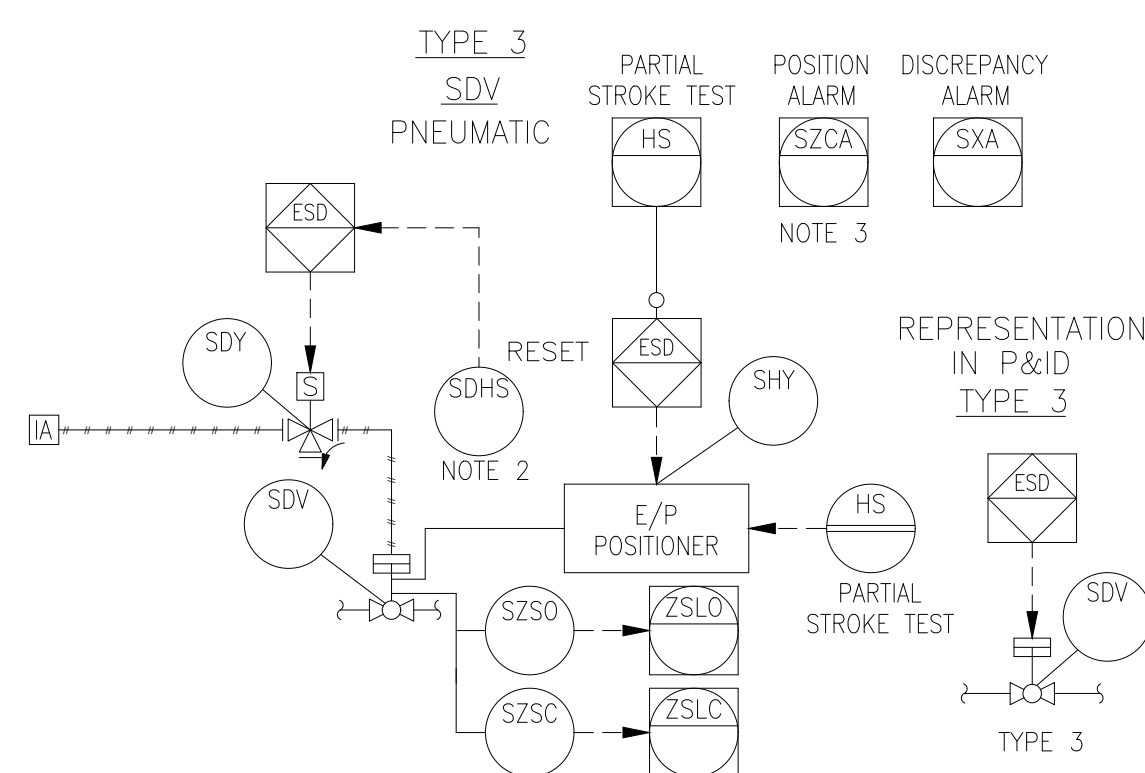
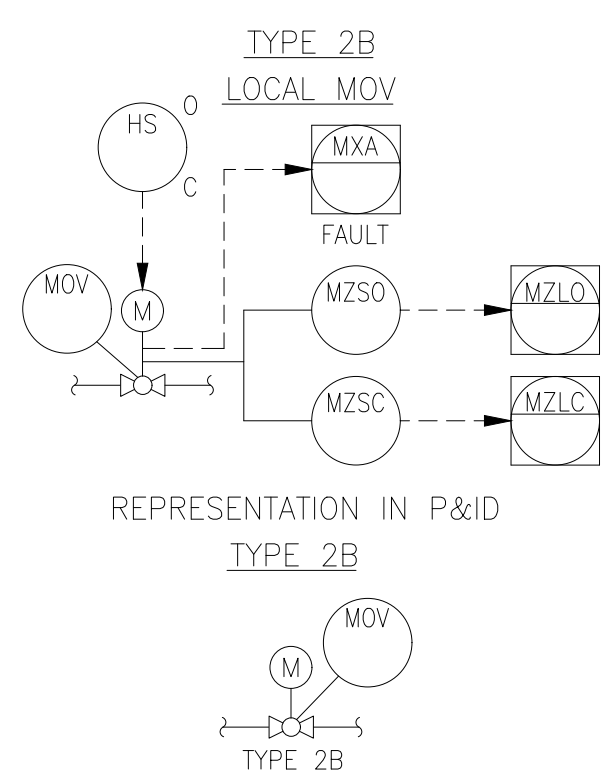
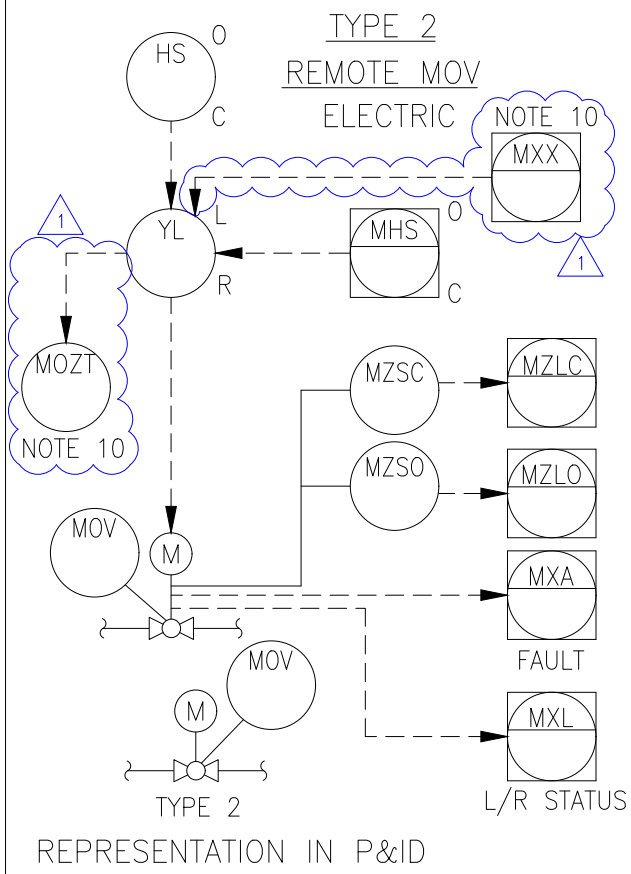
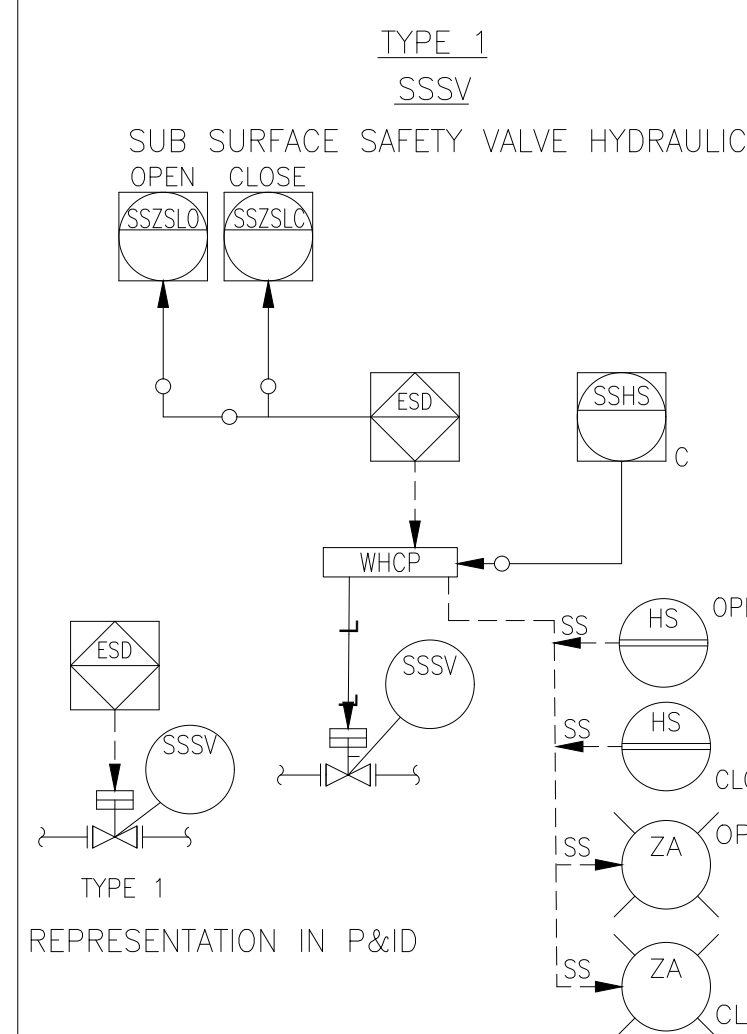
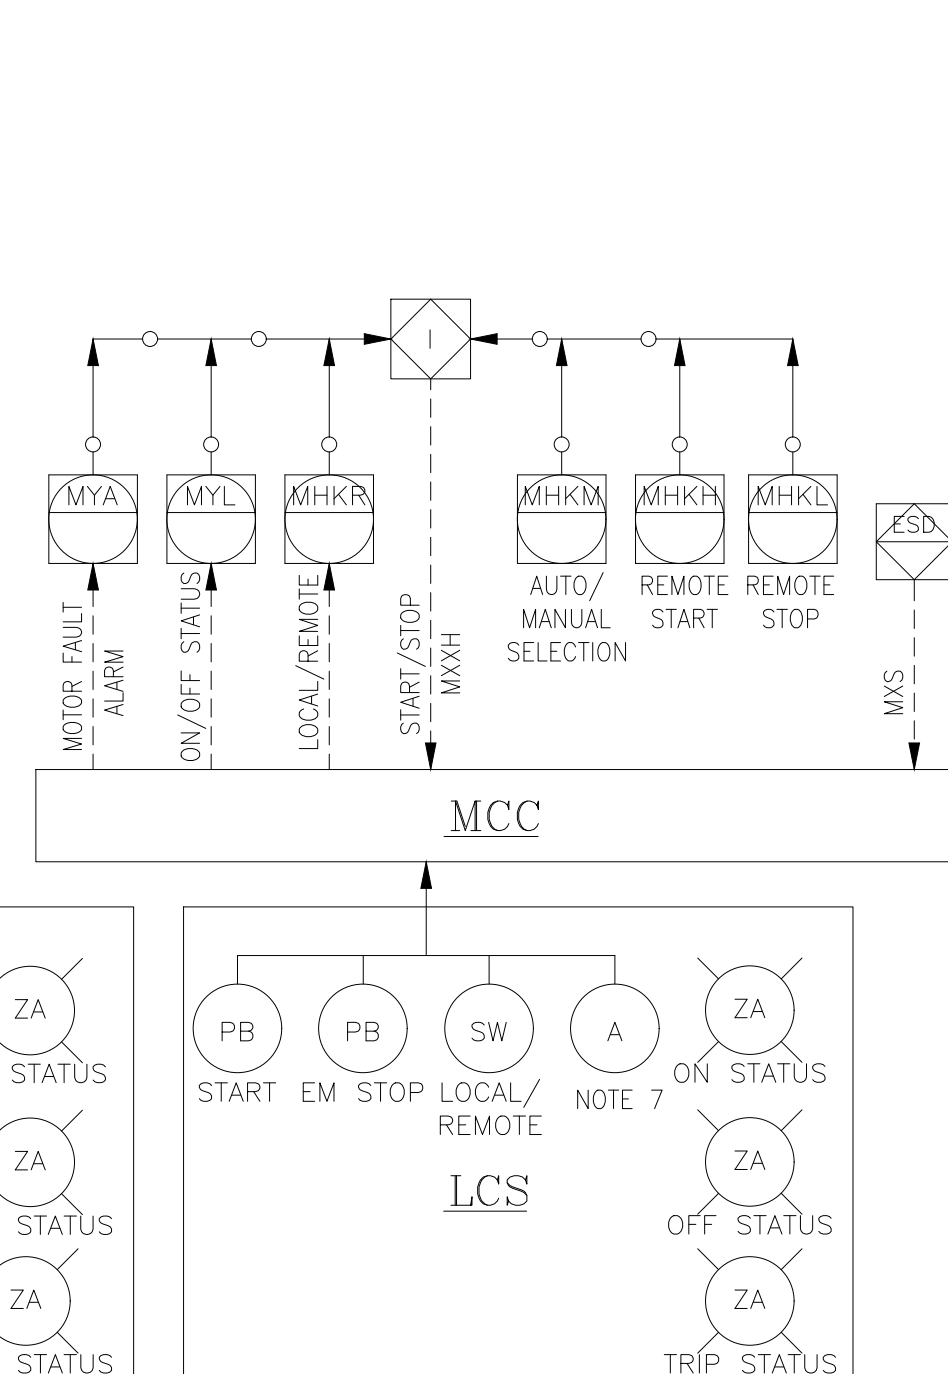
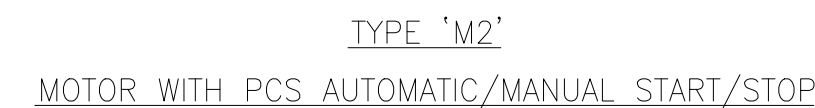
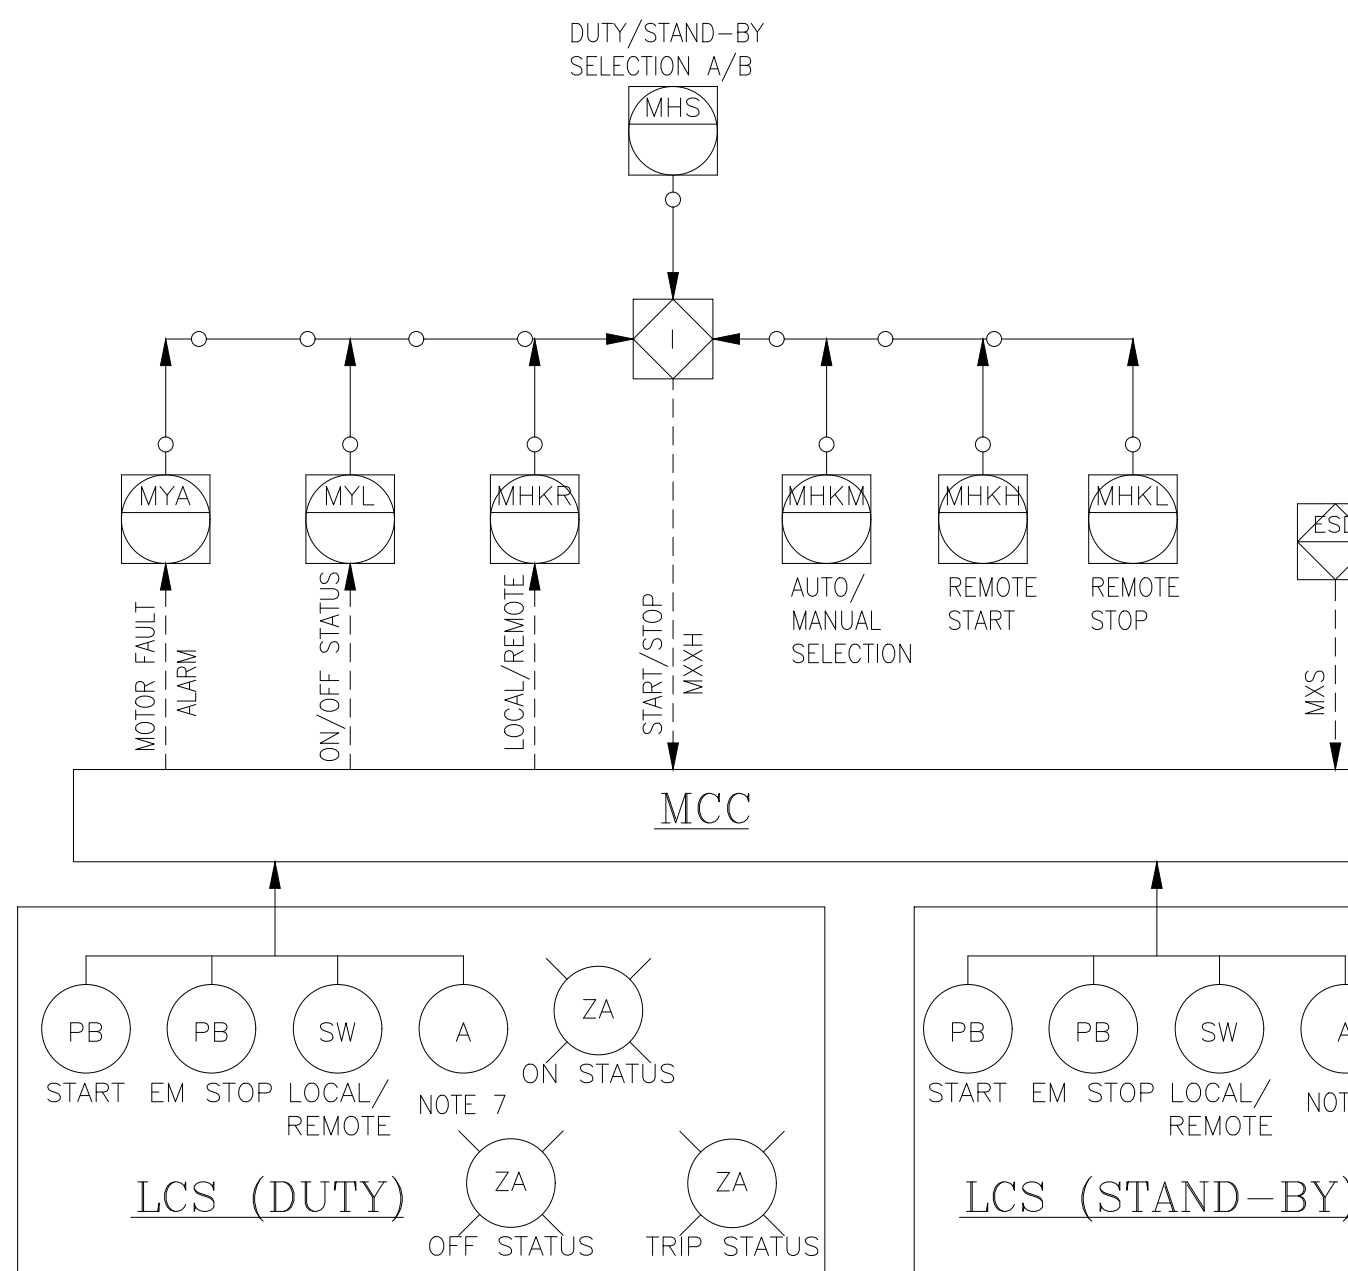
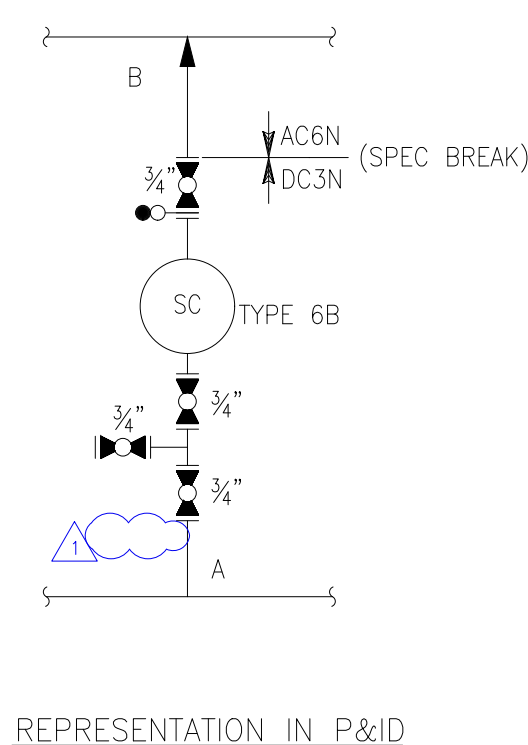
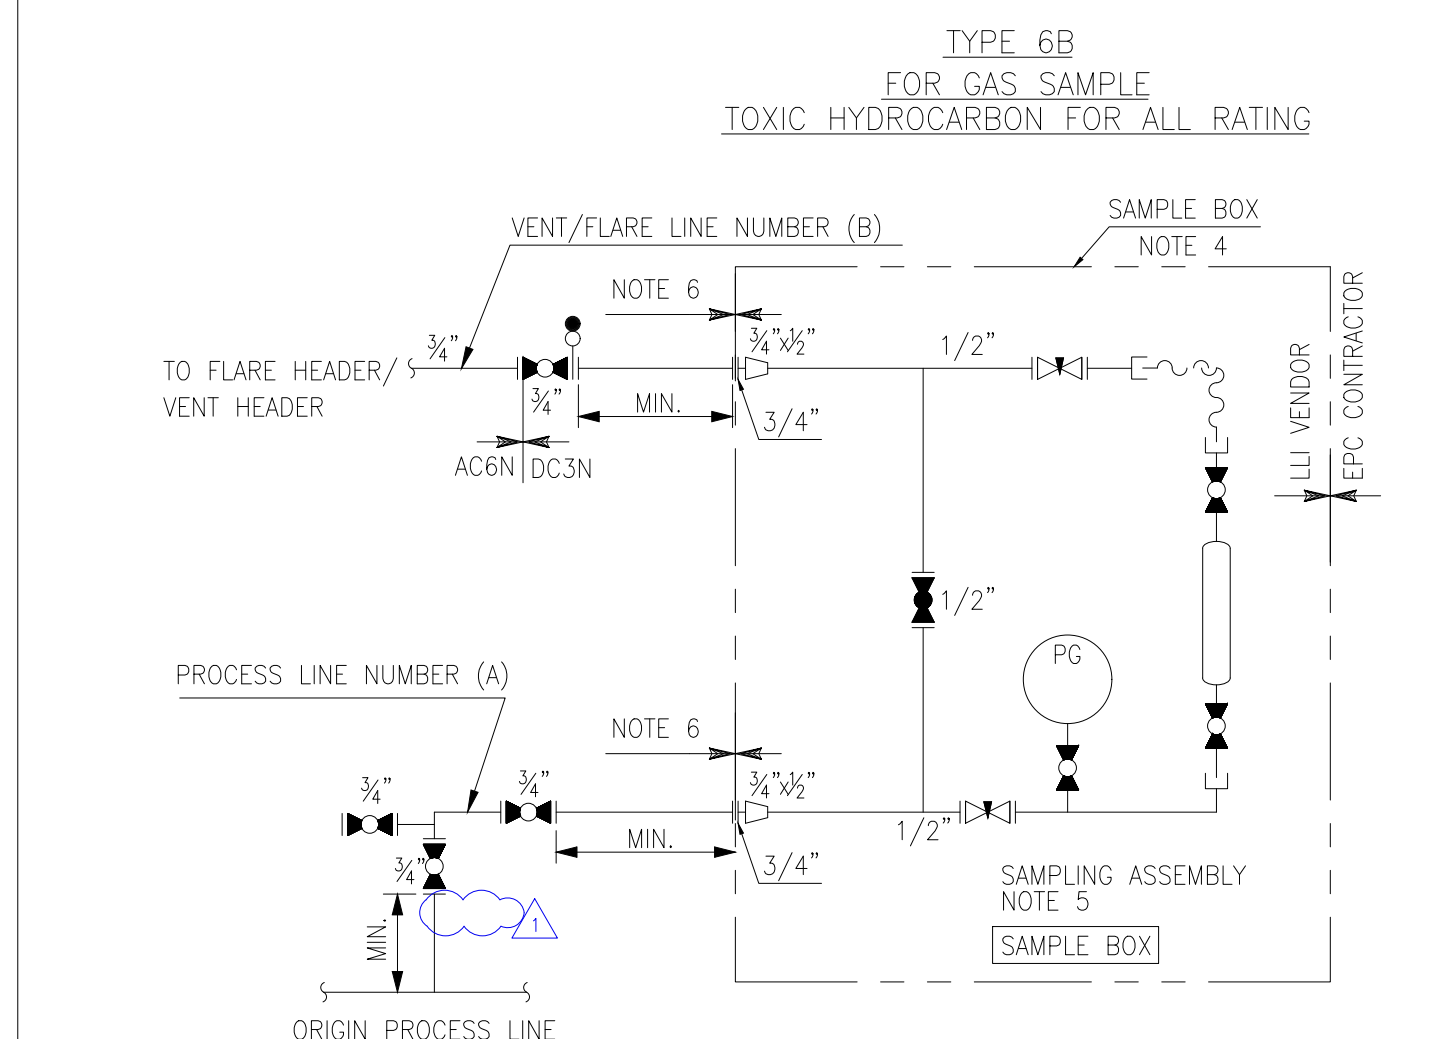


--	--	

TYPICAL ARRANGEMENT FOR VALVES

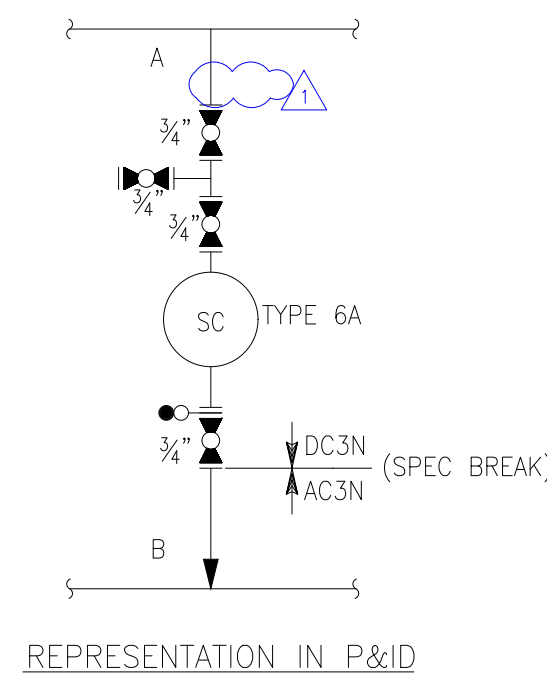

SAMPLE POINT DETAILS

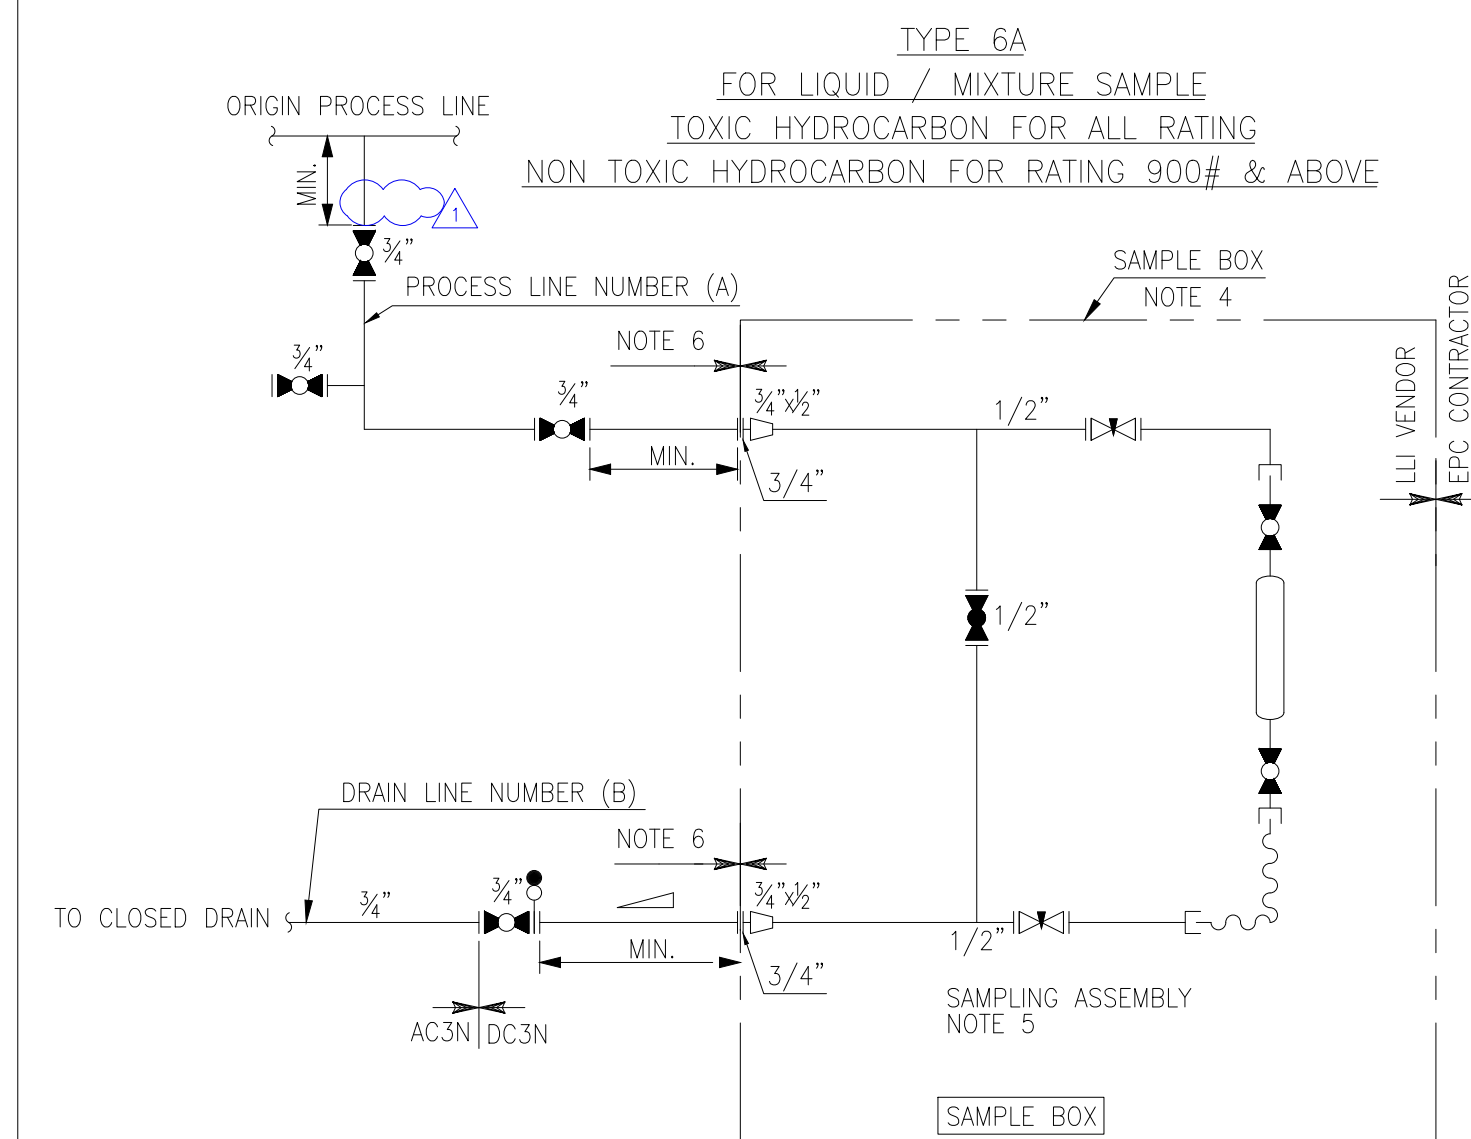

THIS DRAWING HAS BEEN DEVELOPED FROM FEED DRAWING NO. PJ6-DF-CM-BQDA-0001 SHT. 3 REV 1. ALL PORTION DENOTES SCOPE OF WORK UNDER DETAILED ENGINEERING FOR MUBARRAZ REDEVELOPMENT PROJECT
"PJ-2025-CR-002"

1	03/02/2026	RE-APPROVED FOR CONSTRUCTION	SRK	MCS	PK
0	27/11/2025	APPROVED FOR CONSTRUCTION	SRK	MCS	PK
C	17/09/2025	ISSUED FOR DESIGN	RSL	ASL	PK
B	01/08/2025	ISSUED FOR HAZOP	RSL	ASL	PK
A	20/06/2025	ISSUED FOR REVIEW	RSL	ASL	PK
REV.	DATE	DESCRIPTION	DR'N	CH'D	AP'D
SCALE: NTS		LOCATION: MUBARRAZ	COMPANY PROJECT NO PJ-2025-CR-002		

ENGINEERING CONSULTANT:

REJLERS REJLERS TOWER 15TH FLOOR
HAMDAN STREET, PO BOX 39317
ABU DHABI, UAE

ENG CONSULTANT PROJECT NO: 5901055

PMC : DORSCH HOLDING GmbH - ABU DHAB

COMPANY:

ABU DHABI OIL CO., LTD


PROJECT:
DETAILED ENGINEERING FOR MUBARRAZ REDEVELOPMENT PROJECT
(EPC PHASE)

DRG. TITLE:	PIPING AND INSTRUMENTATION DIAGRAM LEGENDS AND SYMBOLS
-------------	---

DWG. NO.	PJ6-EXD-GEN-BQDA-0002	REV NO.	SHEET NO.
		1	003

Filename : PJ6-EXD-GEN-BQDA-0002-003_1.DWG

SHT SIZE: A1

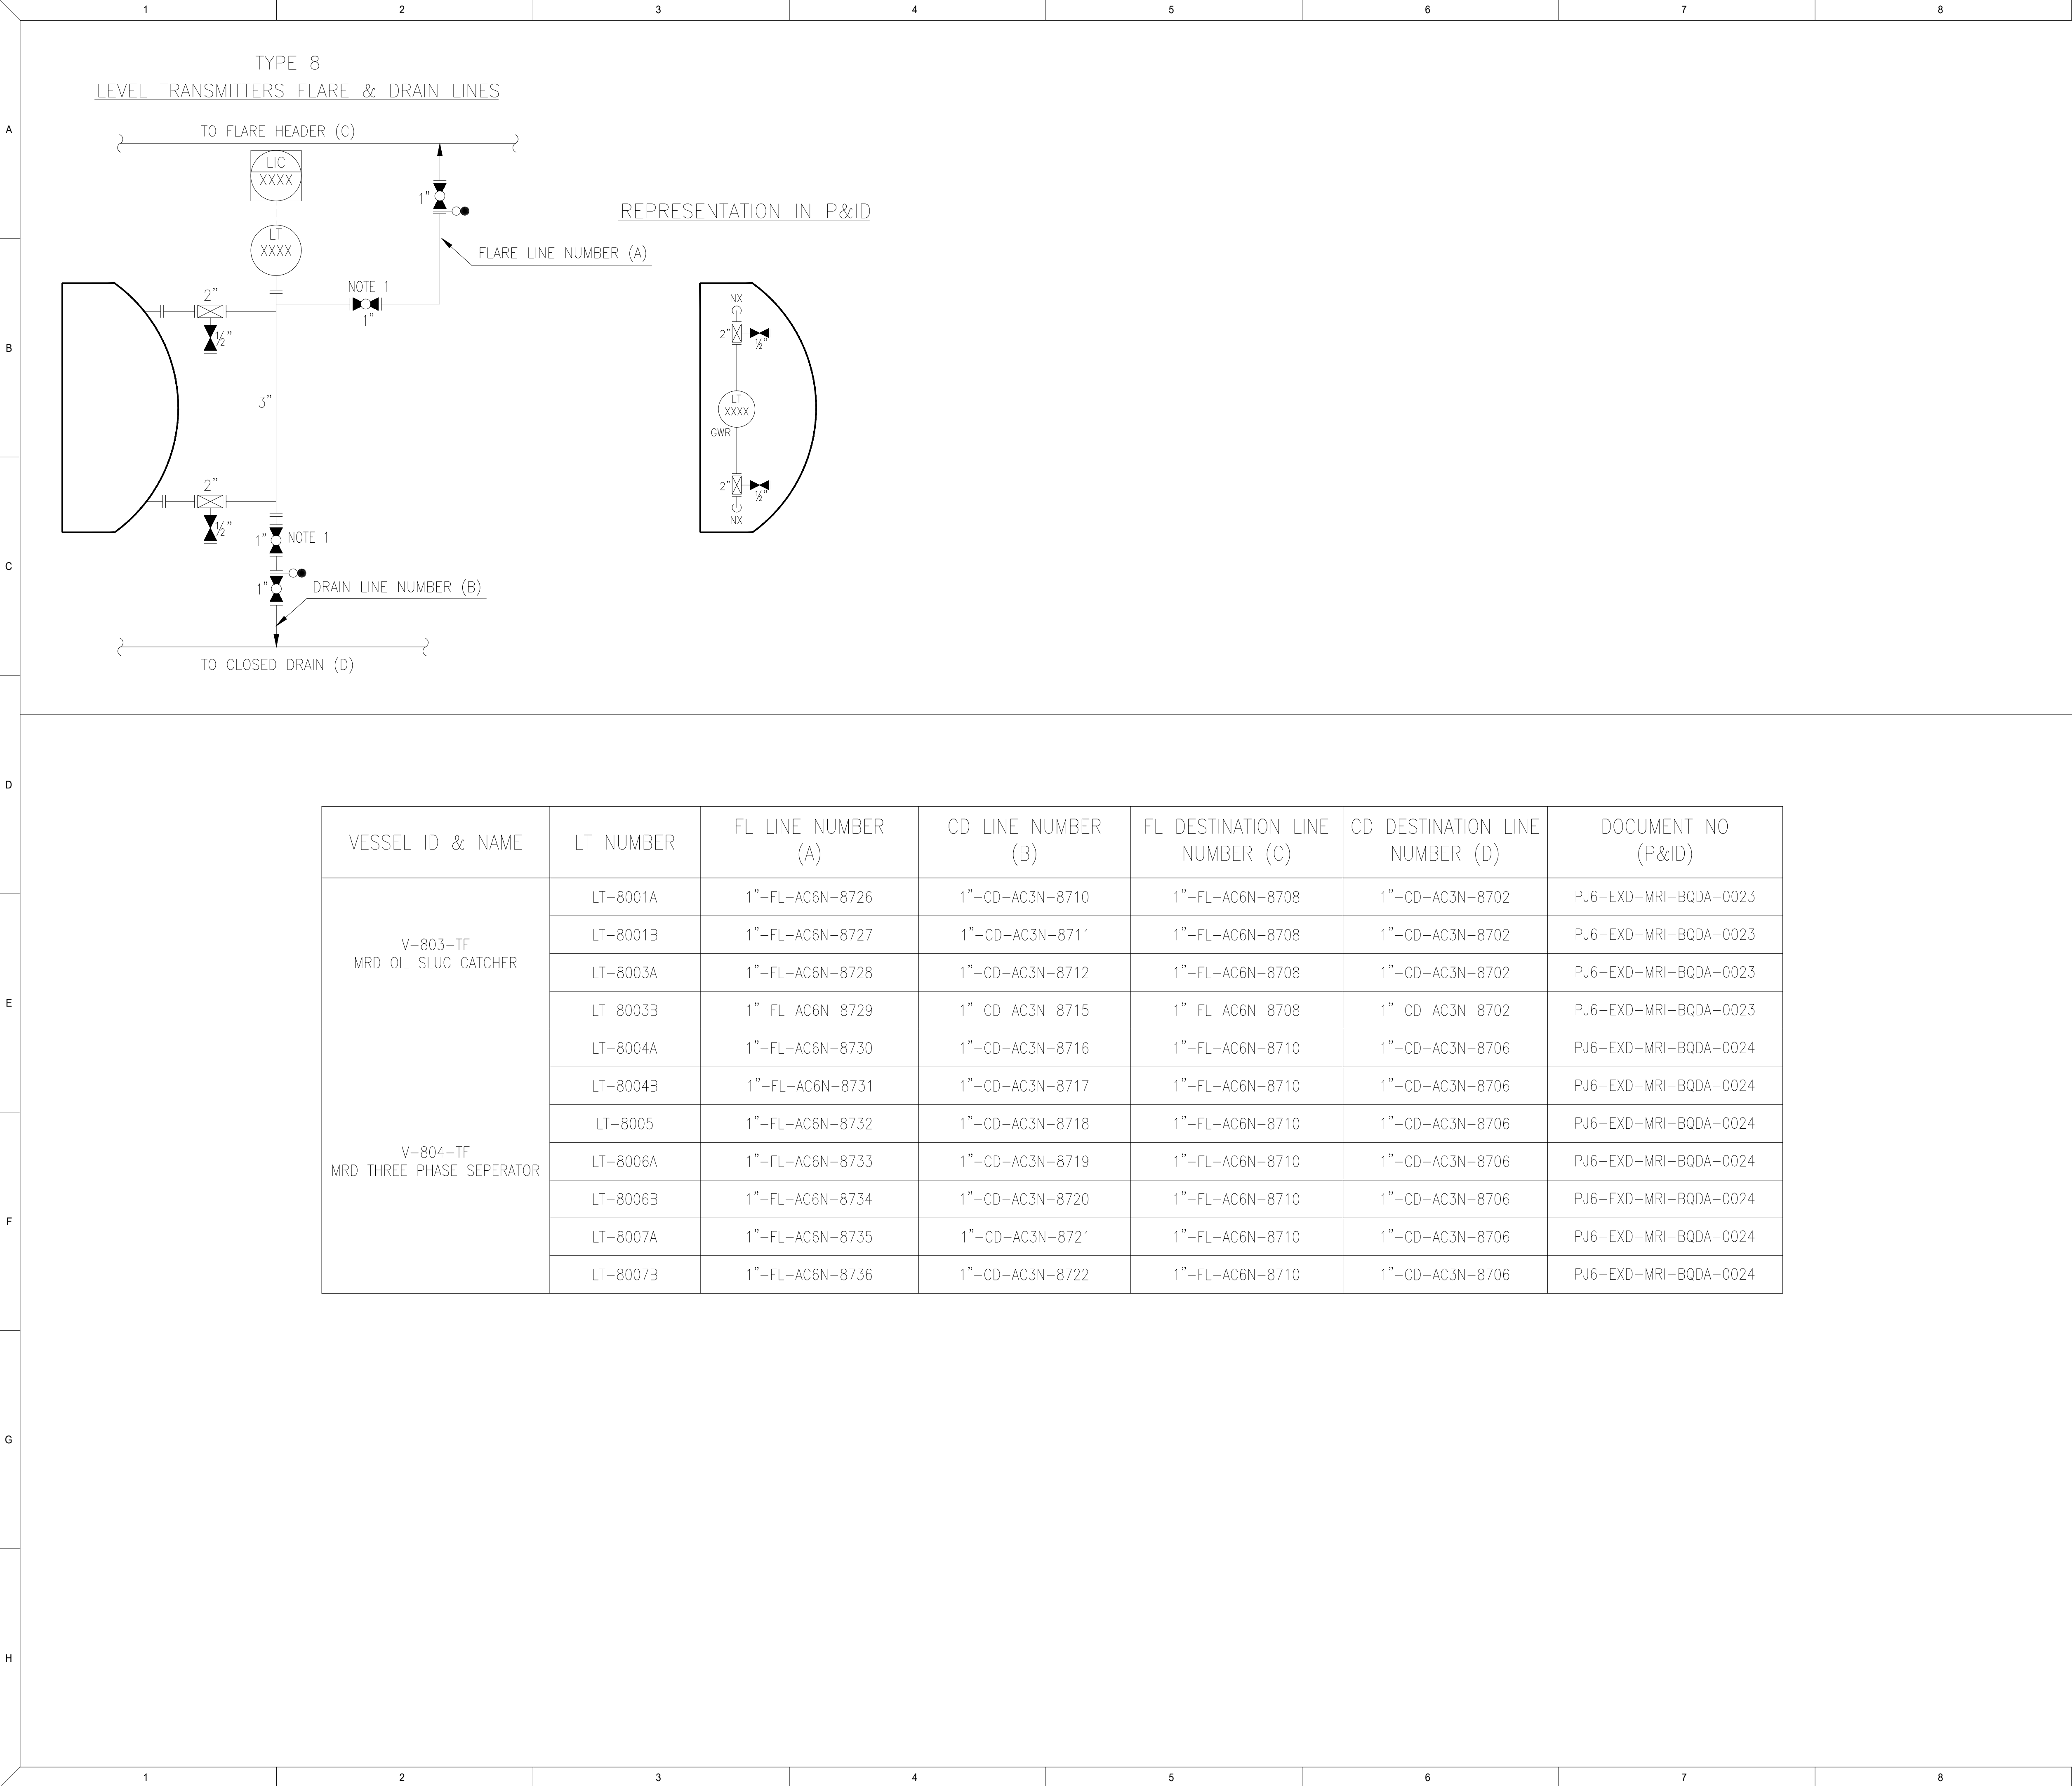

NOTES

1. LG AND LT INSTRUMENT ISOLATION DBB, VENT AND DRAIN VALVE SCOPE DETAILS REFER INSTRUMENT HOOKUP DRAWING DOC.NO PJ6-EXD-GEN-YZ0A-0002.

LEGEND

REVISION CLOUD

THIS DRAWING HAS BEEN DEVELOPED FROM FEED DRAWING NO. PJ6-DF-CM-BQDA-0001 SHT. 3 REV 1. ALL PORTION DENOTES SCOPE OF WORK UNDER DETAILED ENGINEERING FOR MUBARRAZ REDEVELOPMENT PROJECT "PJ-2025-CR-002"

1

03/02/2026

RE-APPROVED FOR CONSTRUCTION

SRK

MCS

PKR

0

27/11/2025

APPROVED FOR CONSTRUCTION

SRK

MCS

PKR

C

17/09/2025

ISSUED FOR DESIGN

RSL

ASL

PKR

B

01/08/2025

ISSUED FOR HAZOP

RSL

ASL

PKR

A

20/06/2025

ISSUED FOR REVIEW

RSL

ASL

PKR

REV.

DATE

DESCRIPTION

DR'N

CHD

AP'D

SCALE: NTS

LOCATION: MUBARRAZ

COMPANY PROJECT NO. PJ-2025-CR-002

ENGINEERING CONSULTANT:

REJILERS

REJILERS TOWER 13TH FLOOR
HAMDAN STREET,PO BOX 39317
ABU DHABI, UAE

ENG CONSULTANT PROJECT NO: 5901055

PMC : DORSCH HOLDING GmbH - ABU DHABI

COMPANY:

AD

ABU DHABI OIL CO.,LTD.

PROJECT:

DETAILED ENGINEERING FOR MUBARRAZ REDEVELOPMENT PROJECT (EPC PHASE)

DRG. TITLE:

PIPING AND INSTRUMENTATION DIAGRAM
LEGENDS AND SYMBOLS

DWG. NO.

PJ6-EXD-GEN-BQDA-0002

REV NO.
1

SHEET NO.
004

Filename : PJ6-EXD-GEN-BQDA-0002-004_1.DWG