


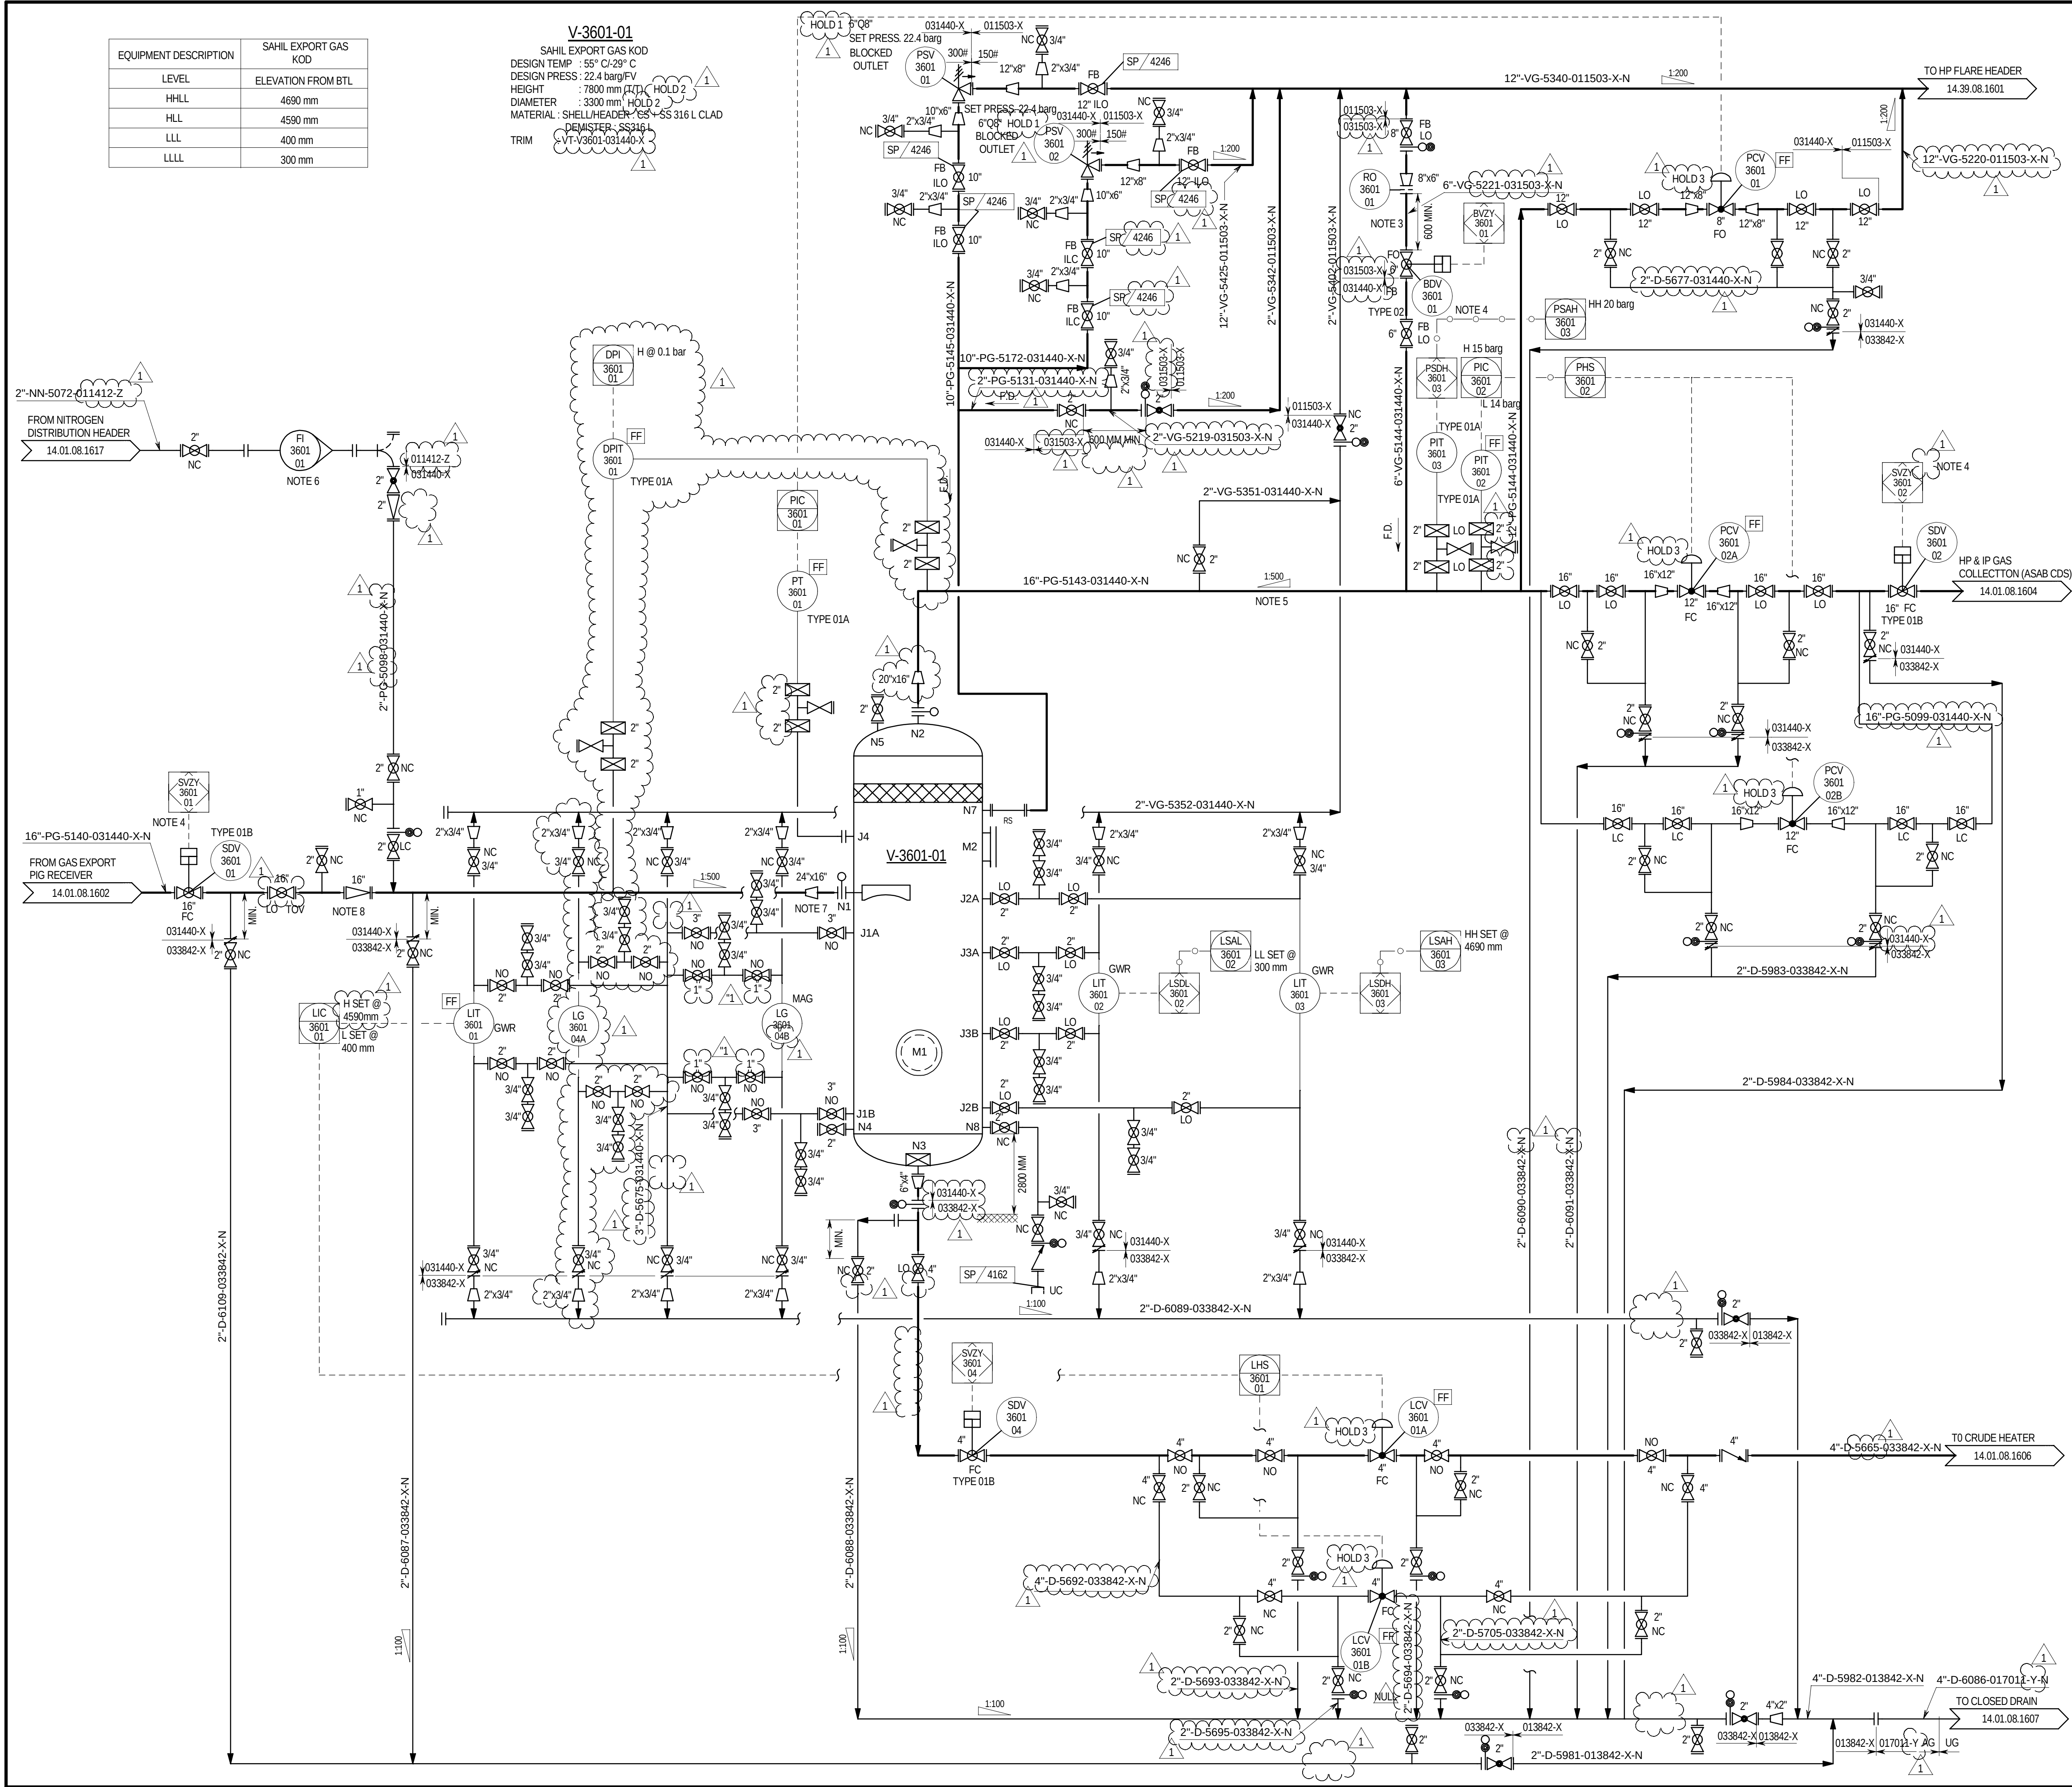

NOTES

1. ALL EQUIPMENT AND INSTRUMENT TAG NUMBERS ON THE DRAWING ARE PREFIXED BY THE AREA CODE (14) AND PLANT AREA CODE (01) UNLESS SPECIFIED OTHERWISE.

2. DELETED.

3. DISCREPANCY ALARM PROVIDED TO INDICATE INADVERTENT OPENING OF BDV DURING NORMAL OPERATION.

4. HIGH HIGH PRESSURE IN EXPORT GAS KOD WILL CLOSE SDV-3601-01 AND SDV-3601-02. SET POINT SHALL BE IN LINE WITH ASAB HP HEADER HH TRIP VALUE.

5. LINE TO BE CONSIDERED FOR 2 PHASE DUE TO ANY LEVEL FAILURE IN KOD.

6. ROTAMETER SHALL BE POSITIONED VERTICALLY UP IN FLOW DIRECTION.

7. 3D STRAIGHT RUN LENGTH REQUIREMENT AT THE UPSTREAM OF INLET NOZZLE.

8. 5D STRAIGHT LENGTH REQUIREMENT AT UPSTREAM OF CHECK VALVE.

HOLDS

1. PSV SIZE

2. VESSEL SIZE

3. CONTROL VALVE SIZE

LEGEND

REVISION CLOUD

DRAWING REFERENCE

TITLE	DRG. NO.
P&ID LEGEND	P16093.30.99.08.1601 SHT. 1 TO 16
PIPING AND INSTRUMENT DIAGRAM SAHIL GAS EXPORT PIG RECEIVER (ASAB CDS)	P16093.14.01.08.1602
PIPING AND INSTRUMENT DIAGRAM HP AND IP GAS COLLECTION ASAB CDS	P16093.14.01.08.1604
PIPING AND INSTRUMENT DIAGRAM CRUDE HEATER E-0401 & E-0402 : TRAIN-1 ASAB CDS	P16093.14.01.08.1606
PIPING AND INSTRUMENT DIAGRAM HP FLARE SUB HEADER INLET / OUTLET FACILITIES CDS FLARE : ASAB	P16093.14.39.08.1601

THIS DRAWING IS NEWLY DEVELOPED FOR THIS PROJECT NO.P16093

1	14/10/2024	KRA	ABS	SHA	ISSUED FOR CONSTRUCTION
E	02/08/2024	KRA	ABS	SHA	ISSUED FOR DESIGN
D	05/07/2024	KRA	ABS	SHA	RE-ISSUED FOR HAZOP
C	14/06/2024	KRA	ABS	SHA	ISSUED FOR HAZOP
B	18/04/2024	KRA	ABS	SHA	ISSUED FOR APPROVAL
A	26/03/2024	KRA	ABS	SHA	ISSUED FOR REVIEW
REV.	DATE	DRN.	CHD.	APD.	DESCRIPTION

SCALE: N.T.S

LOCATION: ASAB

PROJECT No. P16093

ADNOC

ADNOC Onshore

CONSULTANT / CONTRACTOR / VENDOR

REJLERS TARGET

DRAWING No.

PROJECT: EPC OF SAHIL PHASE 3 DEVELOPMENT PROJECT

DRG. TITLE: PIPING AND INSTRUMENT DIAGRAM SAHIL EXPORT GAS KOD ASAB CDS

DRG. No.	14	01	08	1603	1	1/1
AREA	PIAREA	DOC. CODE	SERIAL No.	REV	SHT	OF

P16093-14-01-08-1603-1.PID

2017 ADNOC Onshore . All rights reserved. Abu Dhabi Company for Onshore Petroleum Operations Ltd. Restricted Circulation