


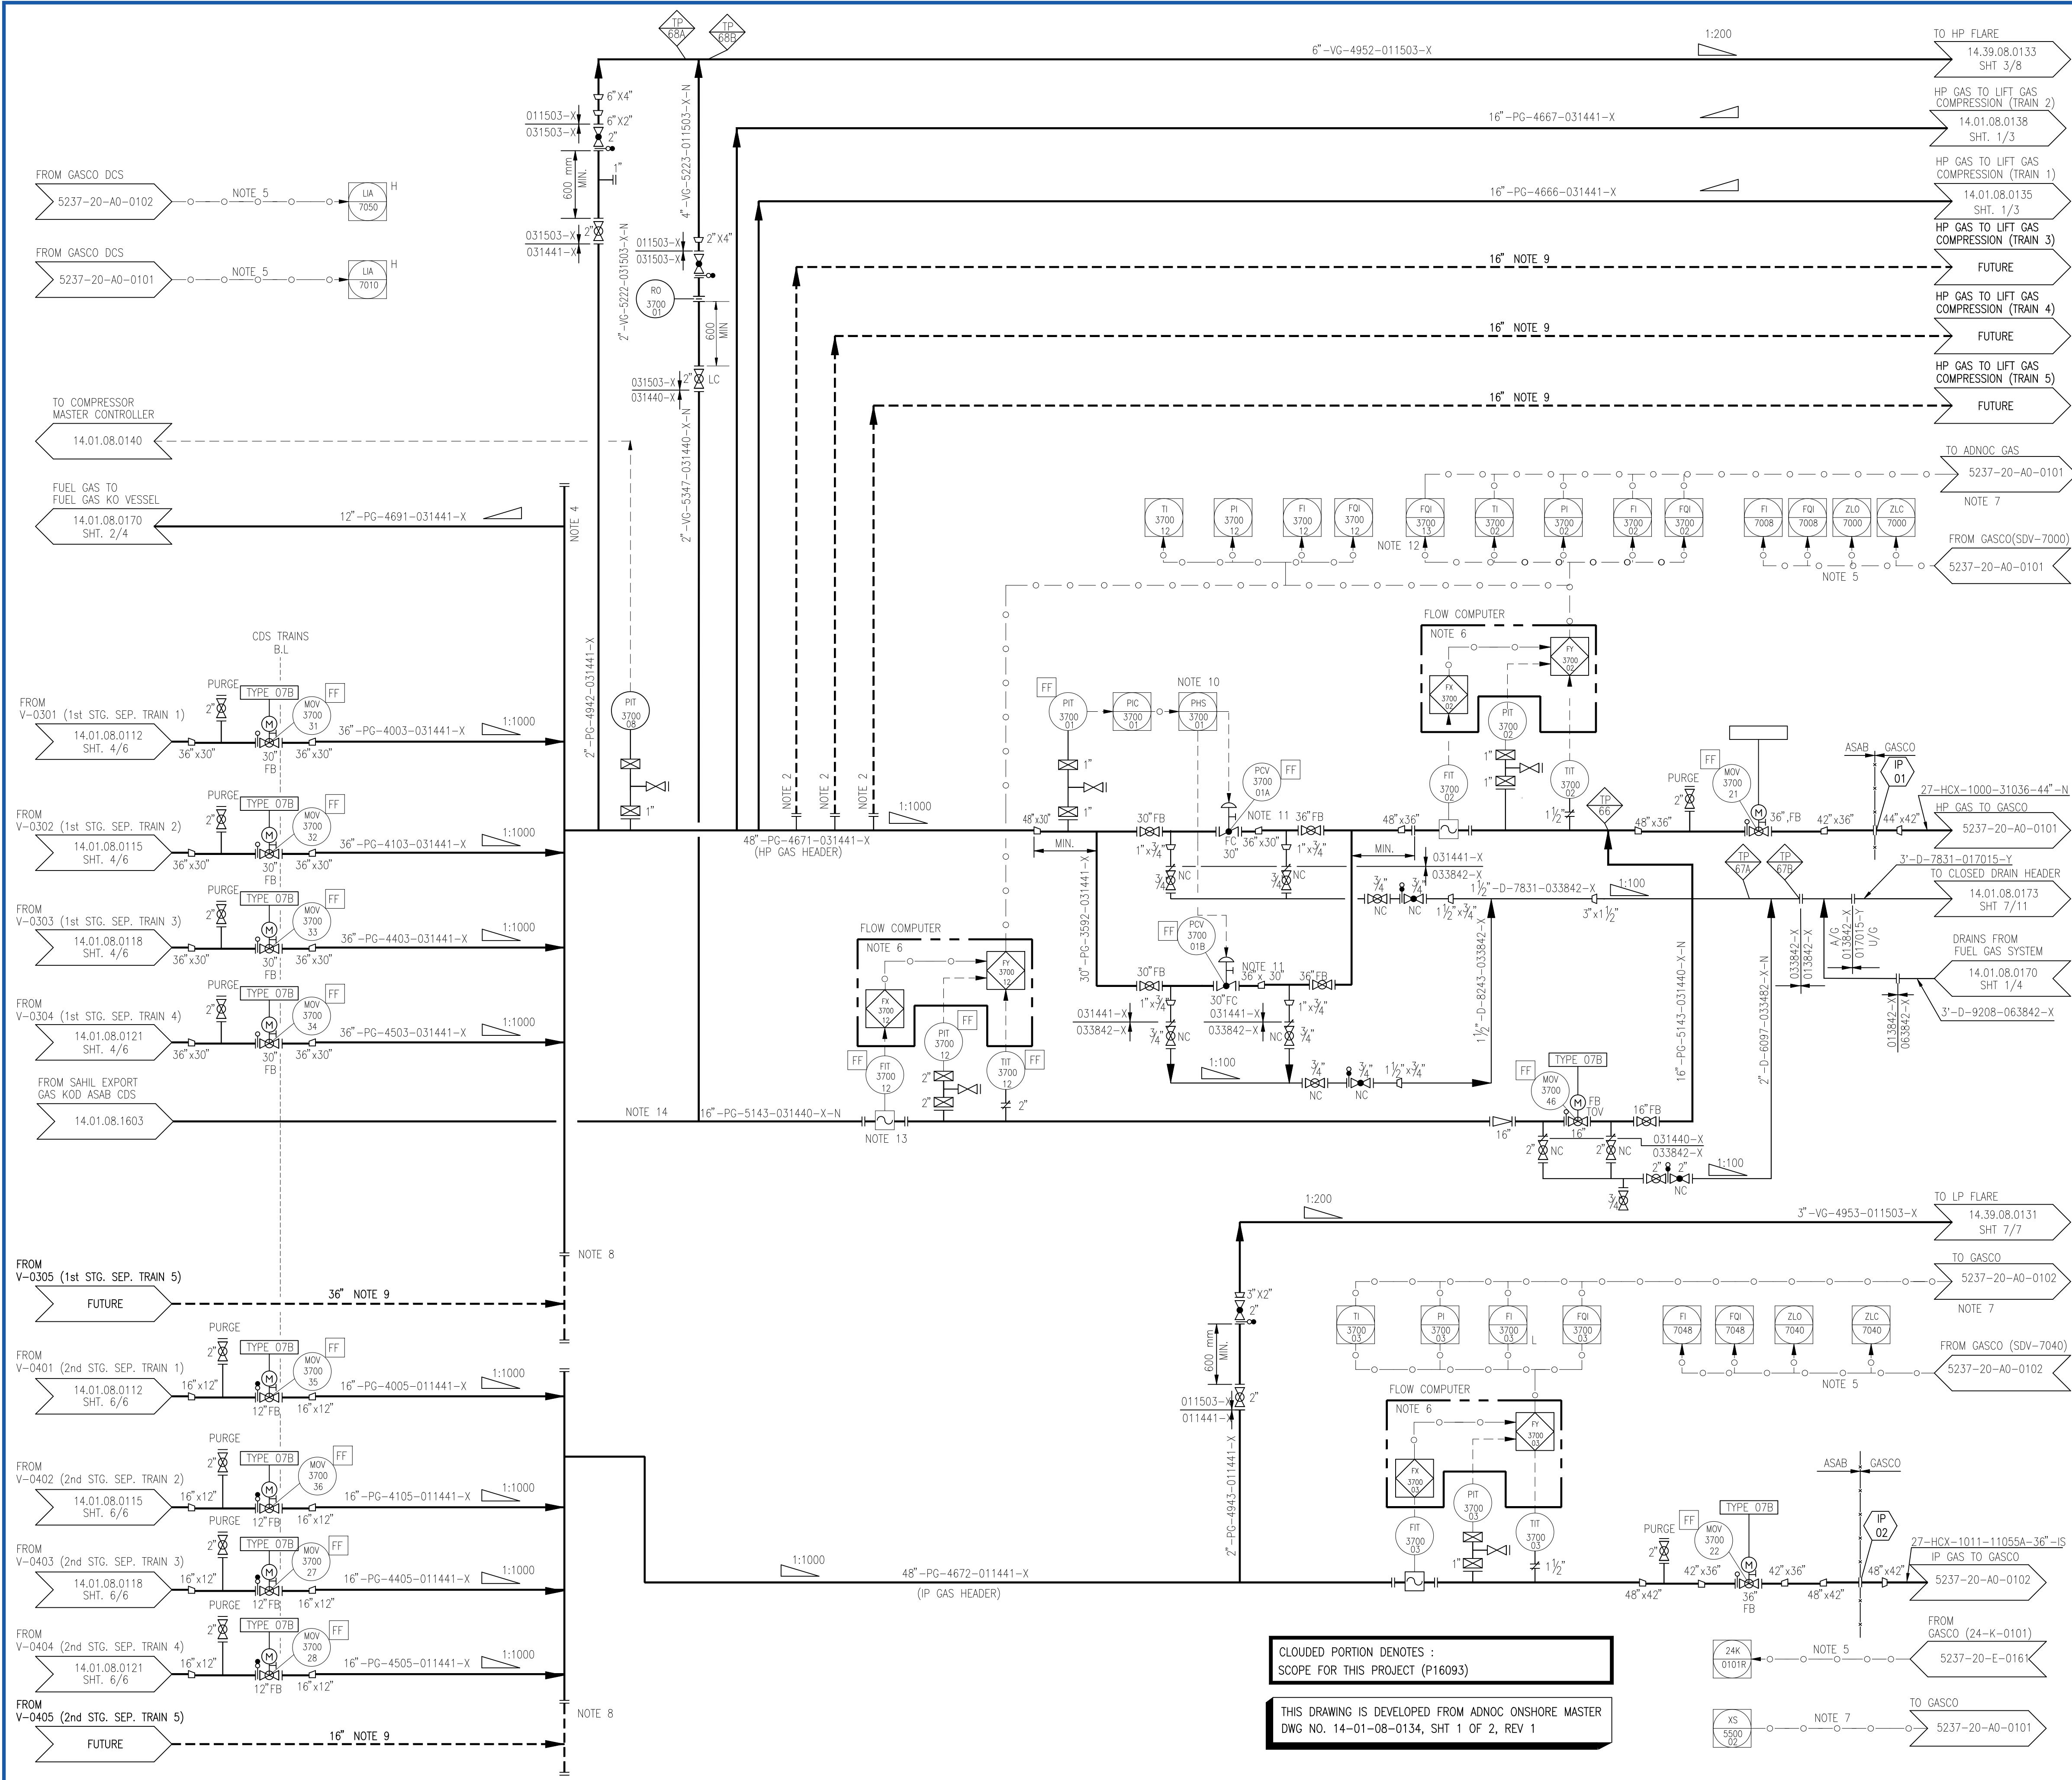

NOTES									
1. ALL EQUIPMENT AND INSTRUMENT TAG NUMBERS ON THE DRAWING ARE PREFIXED BY THE AREA CODE (14) AND PLANT AREA CODE (01) UNLESS SPECIFIED OTHERWISE.									
2. CONNECTION FOR FUTURE GAS LIFT COMPRESSION TRAINS.									
3. COUPON PROBE IS SUITABLE TO MONITOR BOTTOM OF LINE CORROSION.									
4. BRANCH TO BACKUP FUEL GAS IS FROM TOP OF HP GAS HEADER.									
5. SERIAL LINK FROM GASCO.									
6. DEDICATED FLOW COMPUTER IS PROVIDED WITH SERIAL INTERFACE TO DCS.									
7. SIGNALS IS TRANSFERRED FROM ASAB CDS TO ADNOC GAS THROUGH EXISTING FO CABLE FROM ASAB CDS TO ADNOC GAS.									
8. CONNECTION FOR FUTURE FIFTH TRAIN.									
9. FUTURE LINE SIZES (PHASE 2 AND PHASE 3) ARE TENTATIVELY SHOWN FOR PIPE RACK DIMENSION AND STRUCTURAL DESIGN.									
10. OPERATOR TO SELECT STREAM.									
11. THE HP GAS HEADER BACK PRESSURE CONTROL VALVES PCV-3700-01A AND PCV-3700-01B ARE 2X100% (i.e. ONE OPERATIONAL AND ONE SPARE.)									
12. NEW TAG FQI 3700-13 IS ADDED TO SHOW THE TOTAL FLOW TO ADNOC GAS BY SUMMATION OF FIT-3700-02 & FIT-3700-12.									
13. THE UPSTREAM AND DOWNSTREAM STRAIGHT PIPE LENGTHS OF 15D AND 5D ARE REQUIRED FOR FIT-3700-12 RESPECTIVELY, AS PER THE MANUFACTURER'S RECOMMENDATION.									
14. LINE TO BE CONSIDERED FOR 2 PHASE DUE TO ANY LEVEL FAILURE IN SAHIL EXPORT GAS KOD (14-01-V-3601-01).									
LEGEND									
SCOPE CLOUD FOR PROJECT NO. P16093									
REVISION CLOUD FOR PROJECT NO. P16093									
DRAWING REFERENCE									
TITLE						DRG. No.			
P&ID LEGEND						P16093.30.99.08.1601 SHT 1 TO 16			
P&ID - TYPICAL ARRANGEMENT & DETAIL						14.99.08.0121 TO 14.99.08.0126			
P&ID 1ST STAGE SEPARATOR ST-0301 : TRAIN-1						14.01.08.0112 SHT 4/6			
P&ID 2ND STAGE SEPARATOR V-0401 : TRAIN 1						14.01.08.0112 SHT 6/6			
P&ID 1st STAGE SEPARATOR ST-0302 : TRAIN-2						14.01.08.0115 SHT 4/6			
P&ID 2nd STAGE SEPARATOR V-0402 : TRAIN-2						14.01.08.0115 SHT 6/6			
P&ID SLUG CATCHER ST-0303 : TRAIN-3						14.01.08.0118 SHT 4/6			
P&ID 2ND STAGE SEPARATOR V-0403 : TRAIN-3						14.01.08.0118 SHT 6/6			
P&ID-1ST STAGE SEPARATOR ST-0304 : TRAIN 4						14.01.08.0121 SHT 4/6			
P&ID-2ND STAGE SEPARATOR V-0404 : TRAIN-4						14.01.08.0121 SHT 6/6			
P&ID-1ST STAGE SUCTION DRUM V-2801 : TRAIN-1						14.01.08.0135 SHT 1/3			
P&ID-1ST STAGE SUCTION DRUM V-2804 : TRAIN-2						14.01.08.0138 SHT 1/3			
P&ID FUEL GAS HEATER E-3202-01/02/03/04/05/06/07/08						14.01.08.0170 SHT 1/4			
P&ID FUEL GAS SYSTEM V-3201						14.01.08.0170 SHT 2/4			
P&ID CLOSED DRAIN COLLECTION HEADER TRAINS 1&2						14.01.08.0173 SHT 7/11			
P&ID HP FLARE HEADER						14.39.08.0133 SHT 3/8			
P&ID LP FLARE HEADER						14.39.08.0131 SHT 7/7			
PIPING AND INSTRUMENT DIAGRAM SAHIL EXPORT GAS KOD ASAB CDS						P16093.14.01.08.1603			
PIPING AND INSTRUMENT DIAGRAM HP AND IP GAS COLLECTION ASAB CDS (DEMOLITION)						P16093-14-01-08-1608			
1 14/10/2024 SYK ABS SHA ISSUED FOR CONSTRUCTION F 29/08/2024 SYK ABS SHA RE-ISSUED FOR DESIGN E 24/07/2024 SYK ABS SHA ISSUED FOR DESIGN D 04/07/2024 SYK ABS SHA RE-ISSUED FOR HAZOP C 30/05/2024 SYK ABS SHA ISSUED FOR HAZOP B 23/04/2024 SYK ABS SHA ISSUED FOR APPROVAL A 17/04/2024 SYK ABS SHA ISSUED FOR REVIEW REV. DATE DR'N. CH'D. AP'D. DESCRIPTION									
SCALE: N.T.S			LOCATION: ASAB				PROJECT No. P16093		
ADNOC أدنوك البرية ADNOC Onshore CONSULTANT / CONTRACTOR / VENDOR JIREJLERS TARGET DRAWING No.									
PROJECT: EPC OF SAHIL PHASE 3 DEVELOPMENT PROJECT									
DRG. TITLE: PIPING AND INSTRUMENT DIAGRAM HP AND IP GAS COLLECTION ASAB CDS									
DRG.No. 1401081604 1 1/1									
AREA P/AREA DOC. CODE SERIAL No. REV. SHT OF SHT									