



LEGEND / SYMBOLS

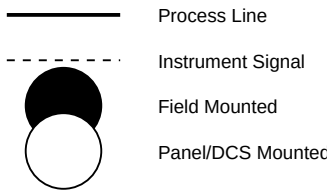

GENERAL NOTES

1. All piping designed per ASME B31.3
2. Instruments per ISA 5.1 standard
3. Pneumatic supply: 6 BARG
4. PSV sized per API 520/521
5. All ratings at design temperature

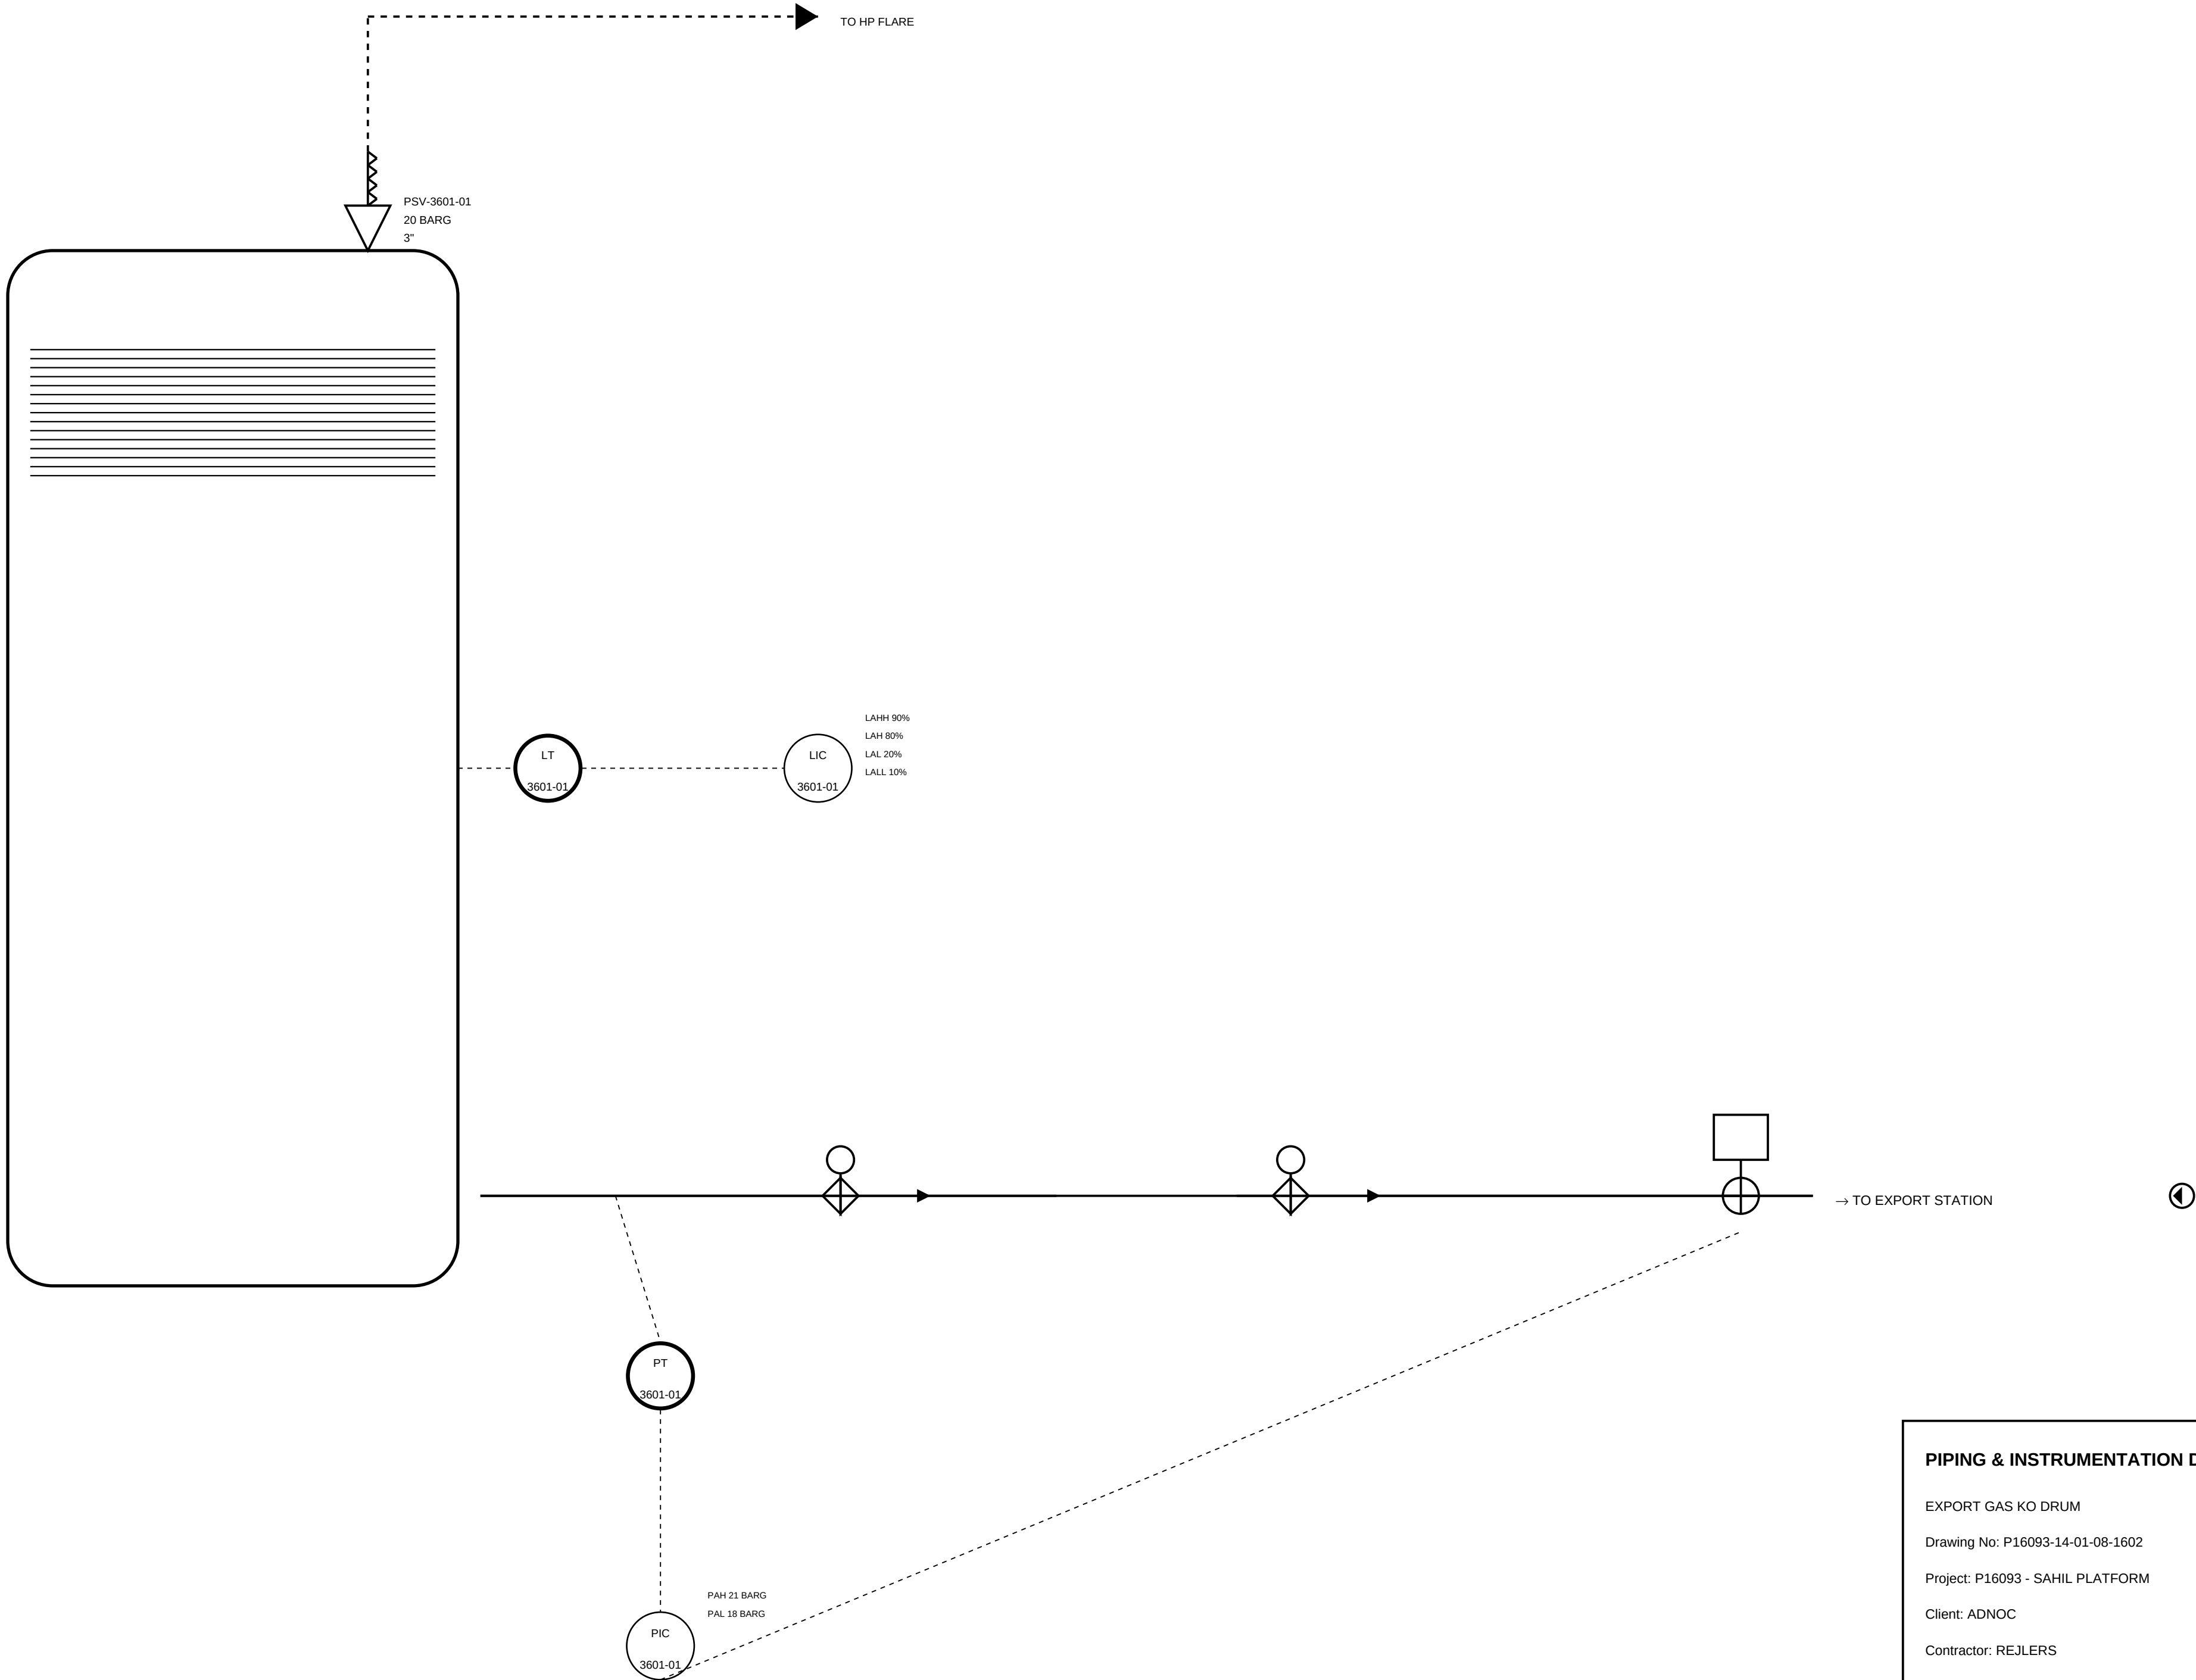

PIPING & INSTRUMENTATION DIAGRAM

EXPORT GAS KO DRUM

Drawing No: P16093-14-01-08-1602

Project: P16093 - SAHIL PLATFORM

Client: ADNOC

Contractor: REJLERS

Rev: A

Date: January 2026